ПОРТФОЛІО · 2026



ОЛЕКСАНДР РІЗНИК

Дизайнер інтер'єрів

Дизайн-концепції, планування, матеріали й оздоблення, презентовані фотореалістичною візуалізацією.

alexriznyk2004@gmail.com

+48 788 818 316 (WhatsApp)

LinkedIn · Telegram

oleksandr-riznyk.vercel.app/ua/interior-designer



Дизайнер інтер'єрів із дипломом бакалавра архітектури та понад 2 роками досвіду в штаті. Розробляв концепції житлових і комерційних приміщень, проєктував шоуруми меблів від концепції до технічних креслень. Готую плани розстановки меблів і освітлення, підбираю матеріали й оздоблення та презентую ідеї фотореалістичною 3D-візуалізацією.

ДОСВІД

CG-художник / 3D-дизайнер

FRANKOF, меблева фабрика · травень 2025 — липень 2026

— Проєктував інтер'єри шоурумів із функціональними зонами під різні колекції — від концепції та візуалізації до технічних креслень.

— Готував проєктну документацію: плани розстановки меблів і планограми, плани освітлення, вбудованих і корпусних меблів, оздоблення стін.

— Вносив правки в проєкт і дистанційно консультував під час ремонту та монтажу меблів.

Дизайнер інтер'єрів / 3D-візуалізатор

MBA Development Group, віддалено · жовтень 2024 — травень 2025

— Розробляв дизайн-концепції житлових і комерційних приміщень — від першої ідеї до візуальної презентації.

— Аналізував наявні приміщення та їхній потенціал, щоб знайти функціональні рішення.

— Підбирав кольорові палітри, оздоблювальні матеріали, текстури, меблі та декор для цілісних інтер'єрів.

НАВИЧКИ

Дизайн-концепції · Планування простору · Дизайн шоурумів · Матеріали й оздоблення · Кольорові палітри · Плани розстановки меблів · Плани освітлення · 3D-моделювання · Читання архітектурних креслень · Archicad · 3ds Max · Corona Renderer · Adobe Photoshop

ОСВІТА

Бакалавр архітектури

Івано-Франківський національний технічний університет нафти і газу

2022 — 2026

МОВИ

Українська (рідна), англійська (B1), польська (A2)



01 / 06

ВІТАЛЬНЯ З ВИДОМ НА САД

Вітальня, побудована навколо виду: панорамне скління в сосновий сад, стінові панелі з дубового шпону зі вставками темного мармуру, сходи з підсвіткою та паперові підвіси над зоною відпочинку.

МОЯ ЧАСТИНА

Концепція інтер'єру та сцена: розстановка, матеріали, світло, рендер. Моделі меблів були готові.

МАТЕРІАЛИ

Стінові панелі з дубового шпону, вставки темного мармуру, бетонна стеля, великоформатна плитка під камінь, джутовий килим, кам'яний журнальний столик, оббивка під замшу.

СВІТЛО

Денне світло зі скління, паперові підвіси, вбудовані точкові світильники, прихована LED-підсвітка під панелями та сходинками, тонкий торшер.

ПРОГРАМИ

3ds Max: сцена й розстановка. Corona Renderer: матеріали, світло, рендер. Photoshop: постобробка.


Анімації камери — на сайті · Повний проєкт на сайті ↗










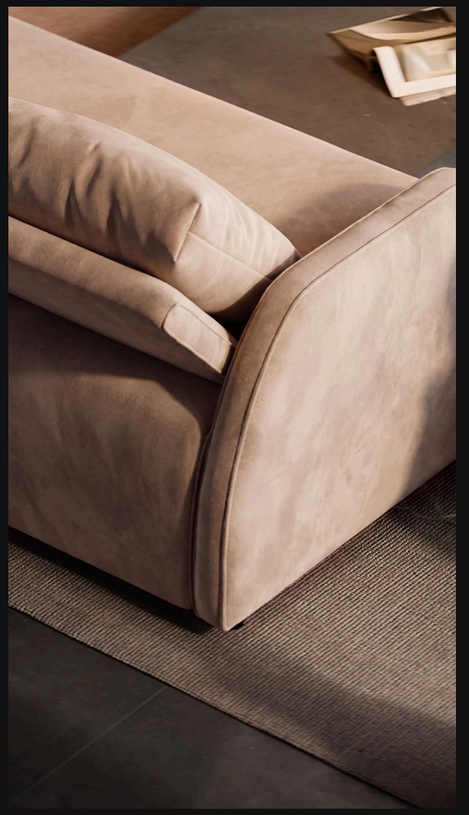

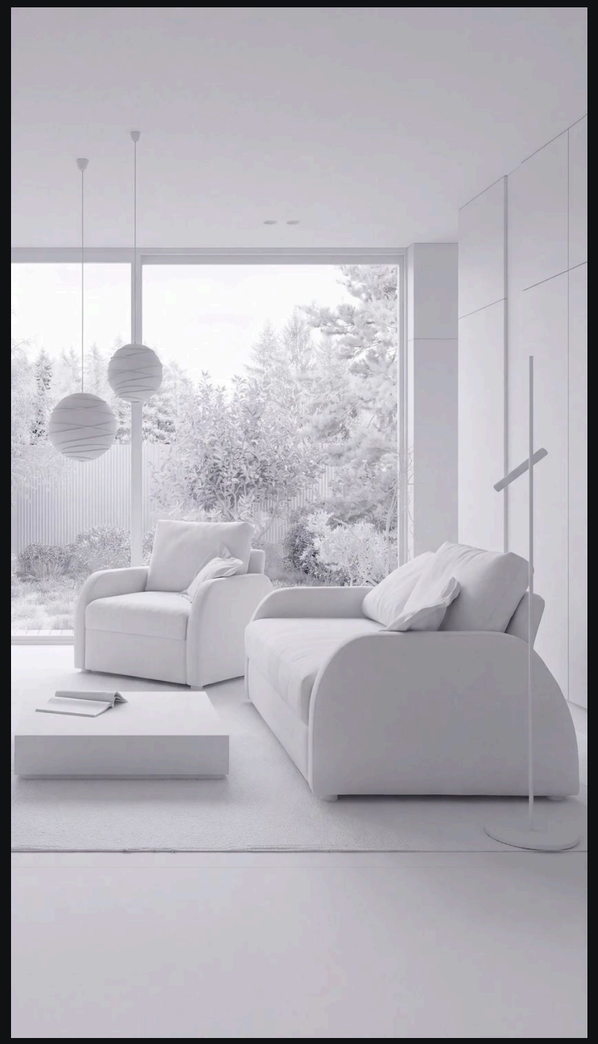









02 / 06

ШОУРУМ FRANKOF

Шоурум меблевої фабрики FRANKOF — від планування в 3ds Max до реалізованого простору. Зал поділений на зони для колекцій спалень, диванів, їдалень і лаунжу, а стелажі-перегородки несуть бренд.

МОЯ ЧАСТИНА

Планування шоуруму: зонування під колекції, розстановка меблів і планограми, перегородки та елементи експозиції, документація для монтажу. Фото реалізованого шоуруму: FRANKOF.

МАТЕРІАЛИ

Стелажі з тонованого в чорне ясена з підсвіченим логотипом, колони в дереві, темні портьєри, графітове ковролінове покриття, зелена акцентна стіна.

СВІТЛО

Чорні трекові споти на відкритій стелі, торшери та настільні лампи в зонах.

ПРОГРАМИ

3ds Max: розстановка, планограми, презентаційні види. Archicad: креслення кольорів стін, світла й фірмових стін.

Повний проєкт на сайті ↗











FRANKOF
FRANKOF

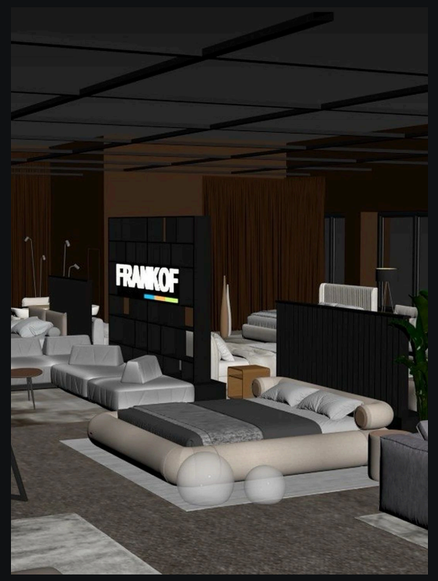
FRANKOF


FRANKOF
FRANKOF


FRANKOF



FRANKOF


FRANKOF
Історія FRANKOF розпочалась 8 жовтня 2009 року. За весь час діяльності компанії ми непохитно переконались: ЛЮДИ - НАША НАЙБІЛЬША ЦІННІСТЬ.
Ми вірємо, що справжня майстерність знаходиться в руках наших працівників, адже на виробництві використовуємо не просто фабричні станки, а й залучаємо українських майстрів, які слідкують за кожним етапом створення виробів.
Ручна робота робить кожен виріб FRANKOF майстерним та унікальним.
Завдяки турботі та досвіду нашої команди Ви інвестуєте у виріб, що слугуватиме Вам роками.


FRANKOF


FRANKOF


КОЛЬОРИ СТІН

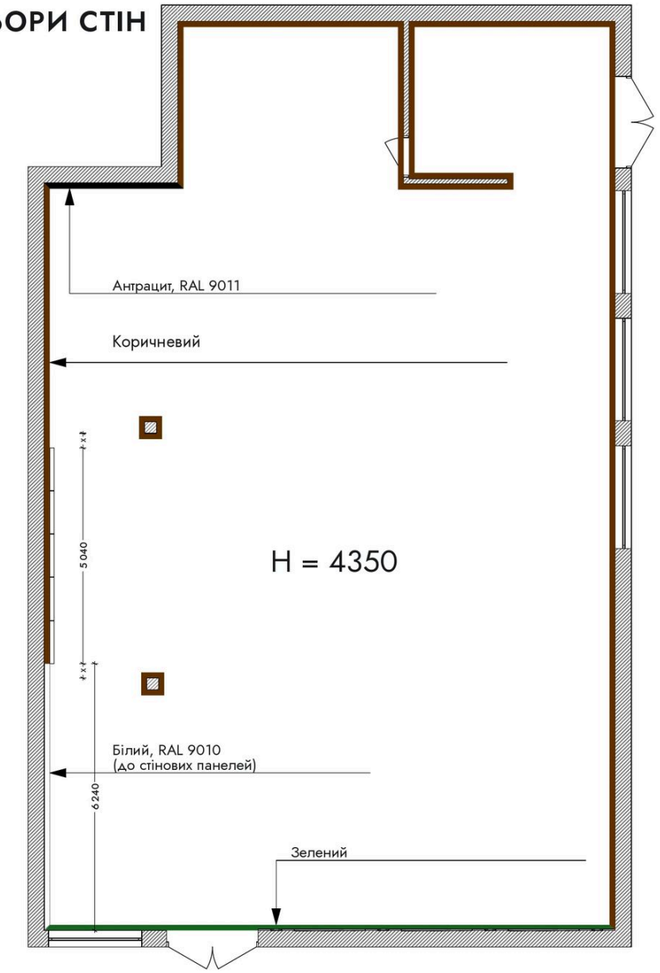

Зелений

Антрацит, RAL 9011

Коричневий

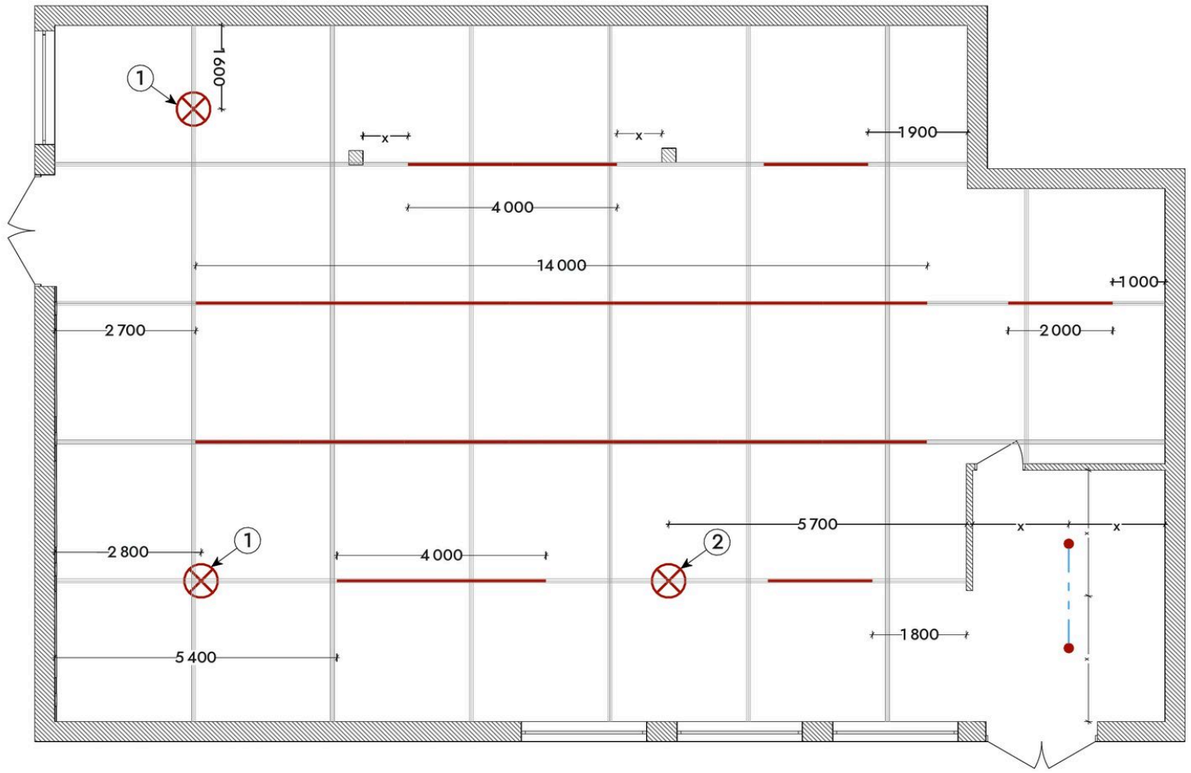

1



2





ПЛАН СВІТЛА

Умовні позначення


- світильник підвісний
- світильник точковий
- світильник трековий

РОЗГОРТКА ФІРМОВОЇ СТІНИ

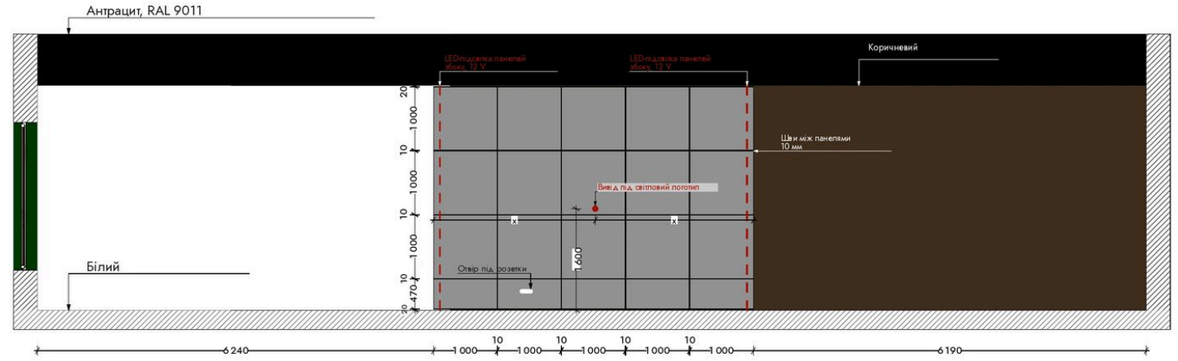

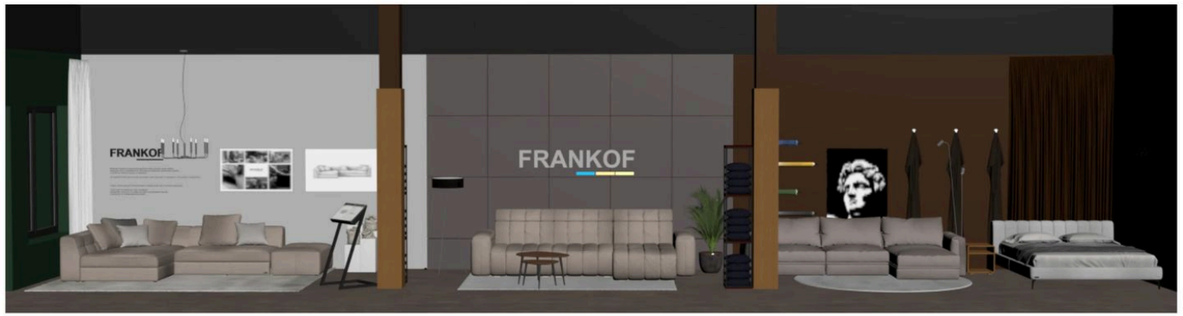

СТІНА З МОЛДИНГАМИ

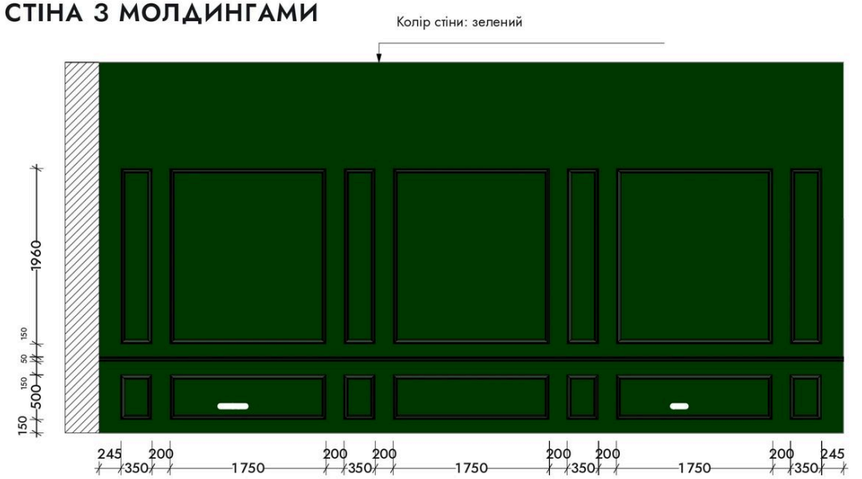





03 / 06

МАНСАРДНА КВАРТИРА

Ціла квартира в мансарді, спроєктована в MBA Development Group: кухня-їдальня, вітальня з каміном, спальня, кабінет і ванна в одній спокійній теплій палітрі.

МОЯ ЧАСТИНА

Дизайн-концепція та візуалізація: зонування, матеріали й оздоблення, підбір меблів і світла, рендер. Робочі креслення не входили в мою частину.

МАТЕРІАЛИ

Дубова підлога ялинкою, світлий кам'яний острів, скляні перегородки в чорному профілі, темні дерев'яні панелі з підсвіткою, камінь навколо каміна, зелені стіни з деревом у кабінеті, бежева штукатурка й горіхова тумба у ванній.

СВІТЛО


Денне світло з мансардних вікон, приховані LED-лінії в нішах і панелях, скульптурні підвіси над обіднім столом.

ПРОГРАМИ

3ds Max: моделювання та сцена. Corona Renderer: матеріали, світло, рендер. Photoshop: постобробка.

Повний проєкт на сайті ↗



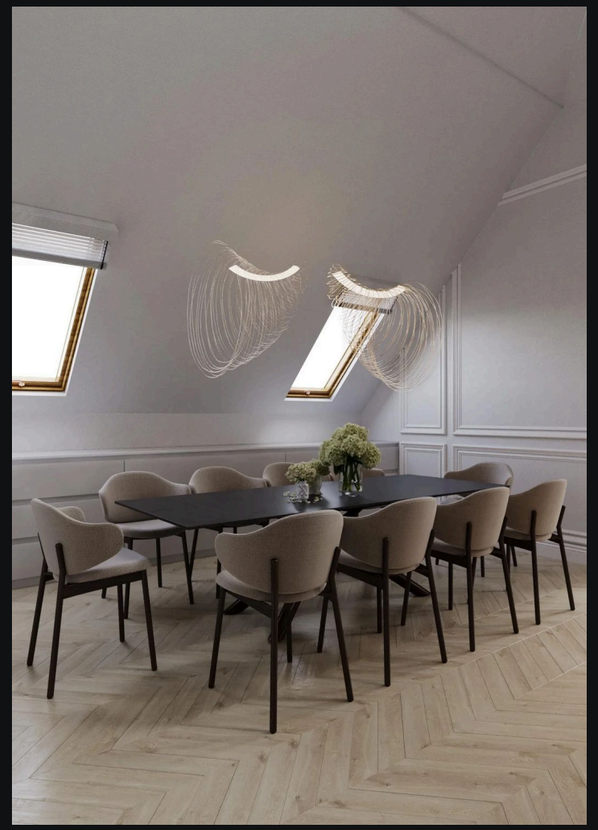


















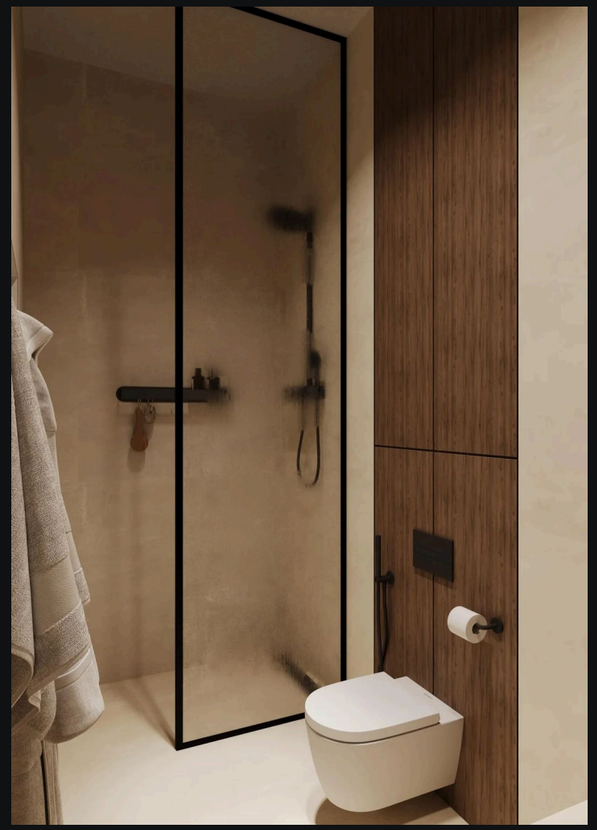





04 / 06

СПАЛЬНЯ «ТИХА РОЗКІШ»

М'яке ліжко й тумба в спокійній спальні з дерев'яними панелями та мармуровою смугою. Одна сцена у двох кольорах велюру, плюс кадр тумби в п'яти тканинах.

МОЯ ЧАСТИНА

Моделювання ліжка, сцена, матеріали, світло, рендер, кінематографічний рух камери. Модель тумби була готова.

МАТЕРІАЛИ

Оббивка: велюр (теракотовий, золотий, шоколадний), шеніл охра, пісочне букле; панелі з темного дуба з підсвіченими кам'яними вставками, мармурова смуга й мармурова плитка на підлозі, лляна постіль, вовняний килим.

СВІТЛО

М'яке денне світло крізь тюль, теплі LED-лінії між панелями, два підвісні світильники над ліжком.

ПРОГРАМИ


3ds Max: моделювання та сцена. Corona Renderer: матеріали, світло, рендер. Photoshop: постобробка. Кінематографічний рух камери зі статичних кадрів.


Анімації камери — на сайті · Повний проєкт на сайті ↗







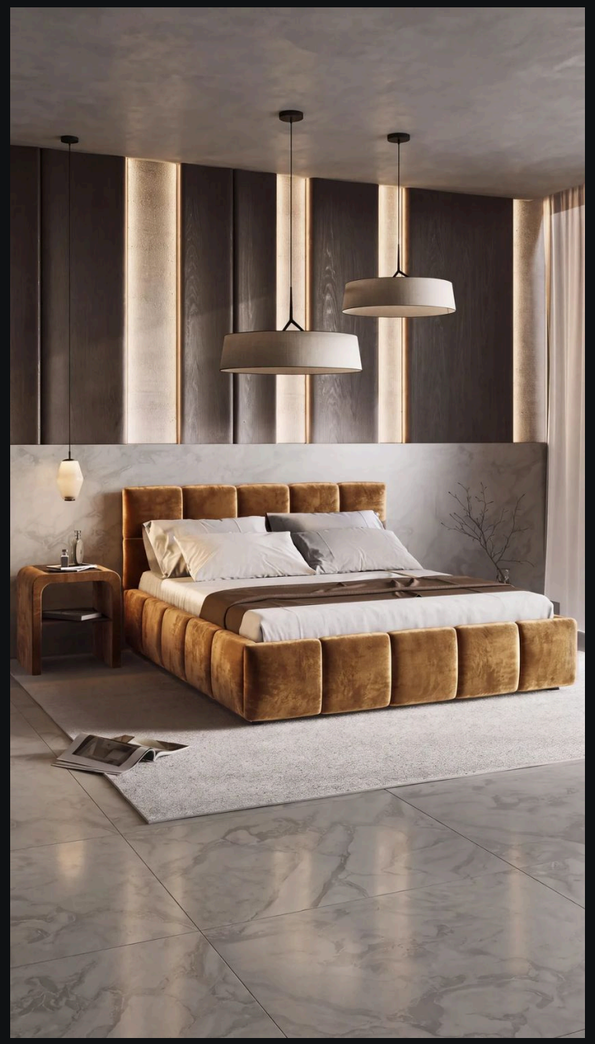

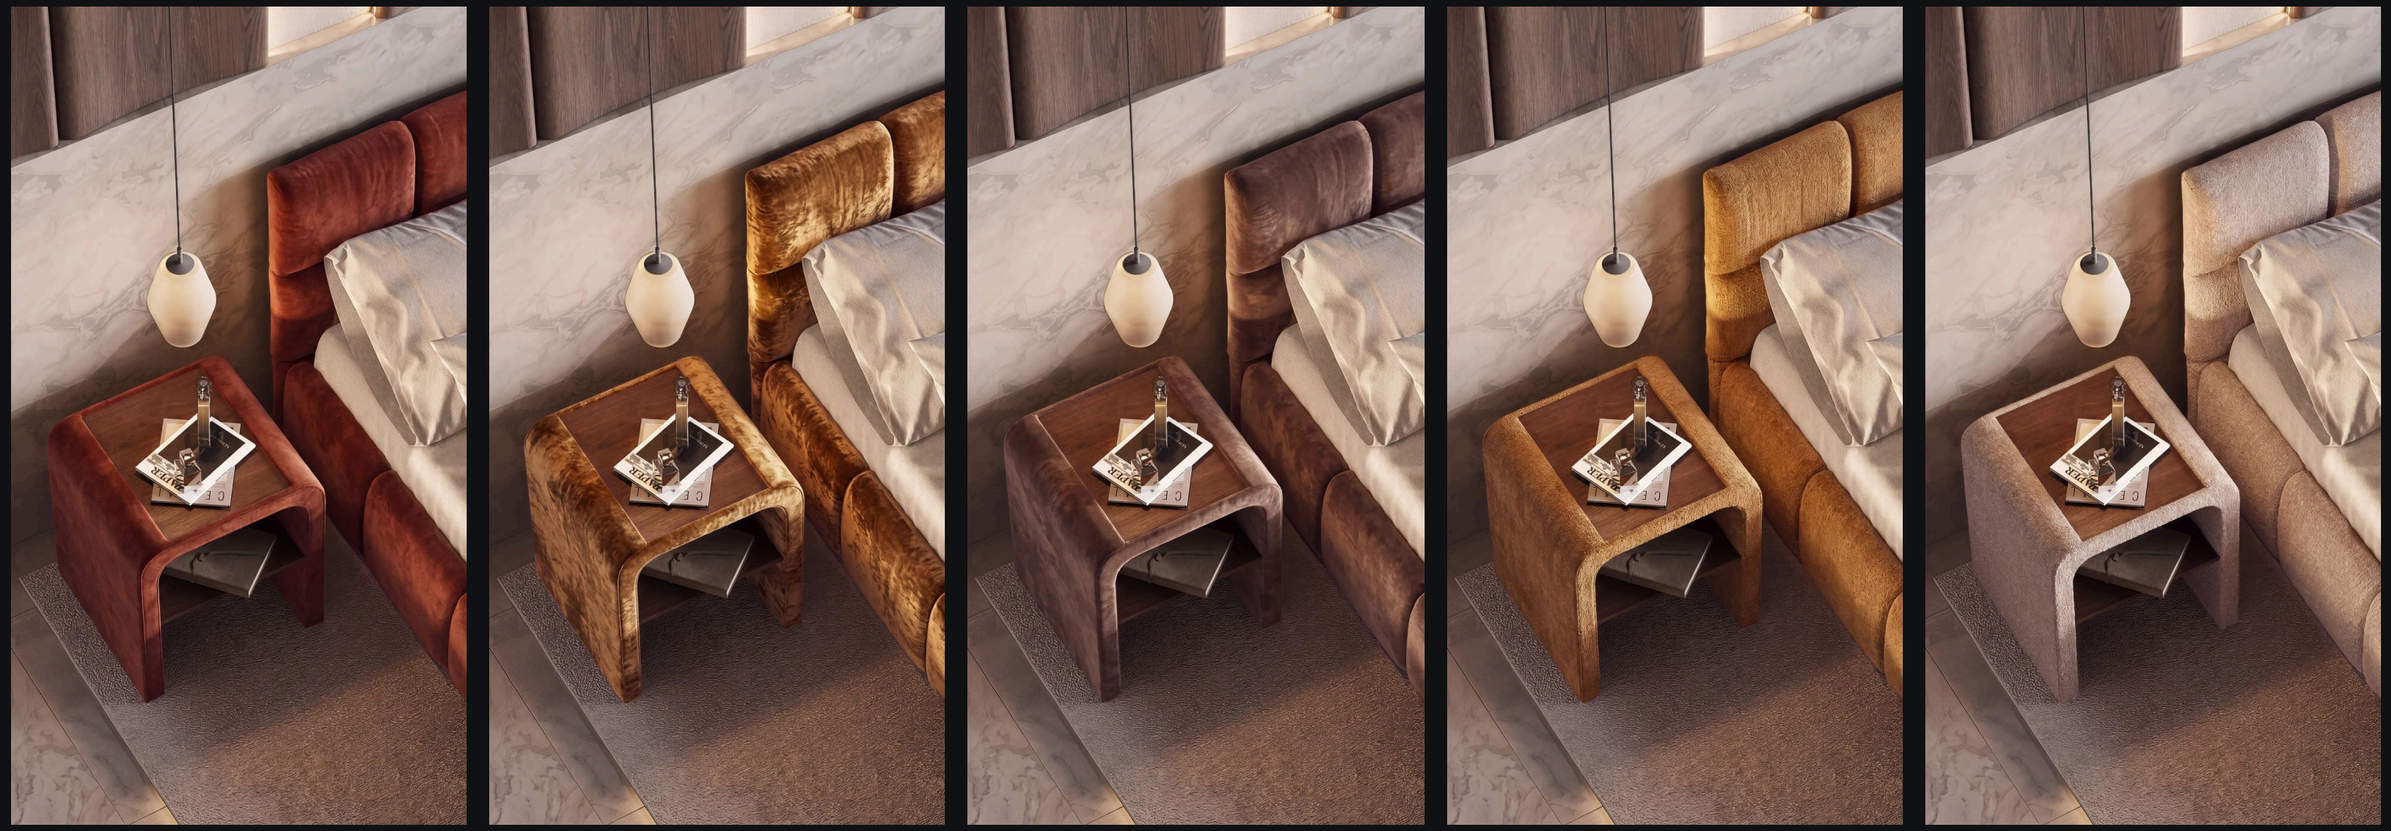



05 / 06

КУХНЯ З ТРАВЕРТИНОМ

Барний стілець у кухні, яку я спроєктував під нього: травертиновий острів, дерев'яні фасади та приховане лінійне світло. Той самий кадр показує п'ять варіантів оббивки.

МОЯ ЧАСТИНА

Концепція та моделювання кухні, матеріали, світло, рендер, кінематографічний рух камери. Модель стільця була готова.

МАТЕРІАЛИ

Травертиновий острів, фасади з дерев'яного шпону, фартух під бетон, дубова підлога, чорні металеві ніжки. Оббивка: велюр, букле, штучне хутро, жакард.

СВІТЛО

Бокове денне світло крізь жалюзі та тепла LED-лінія під навісними шафами.

ПРОГРАМИ

3ds Max: моделювання кухні та сцена. Corona Renderer: матеріали, світло, рендер. Photoshop: постобробка. Кінематографічний рух камери зі статичних кадрів.

Анімації камери — на сайті · Повний проєкт на сайті ↗











06 / 06

ОФІС

Інтер'єр офісу, спроєктований в MBA Development Group: скляна переговорна, обгорнута рейковою дерев'яною перегородкою, і відкрита робоча зона з моховою стіною.

МОЯ ЧАСТИНА

Дизайн-концепція та візуалізація: зонування, матеріали, меблі, рендер. Робочі креслення не входили в мою частину.


МАТЕРІАЛИ


Дерев'яні рейки, безрамне скло, світла дубова підлога, мохова стіна, білі столи.

ПРОГРАМИ

3ds Max: моделювання та сцена. Corona Renderer: матеріали, світло, рендер. Photoshop: постобробка.


Повний проєкт на сайті ↗

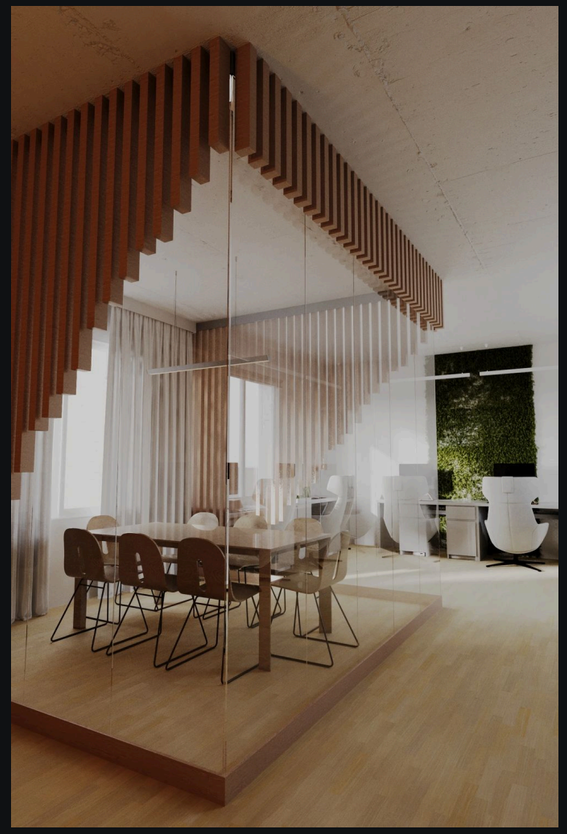

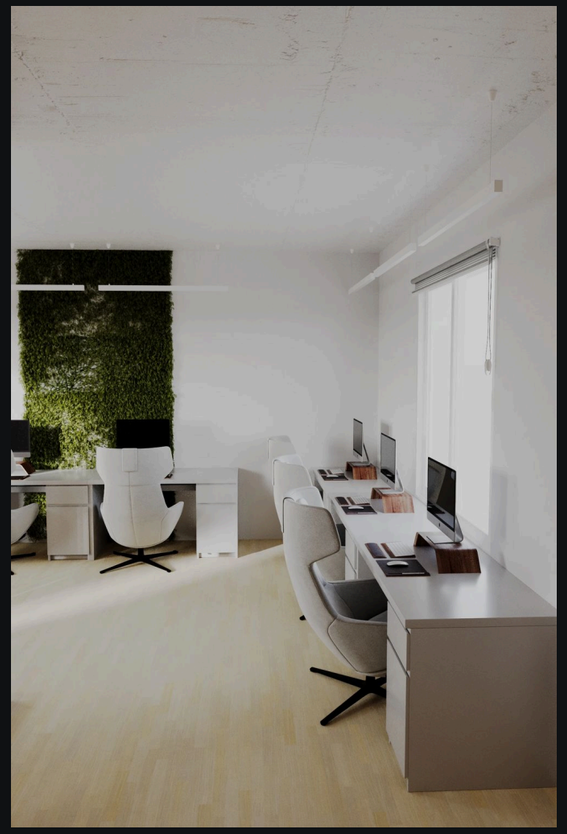




ПЛАН РОЗТАШУВАННЯ МЕБЛІВ
М 1:50

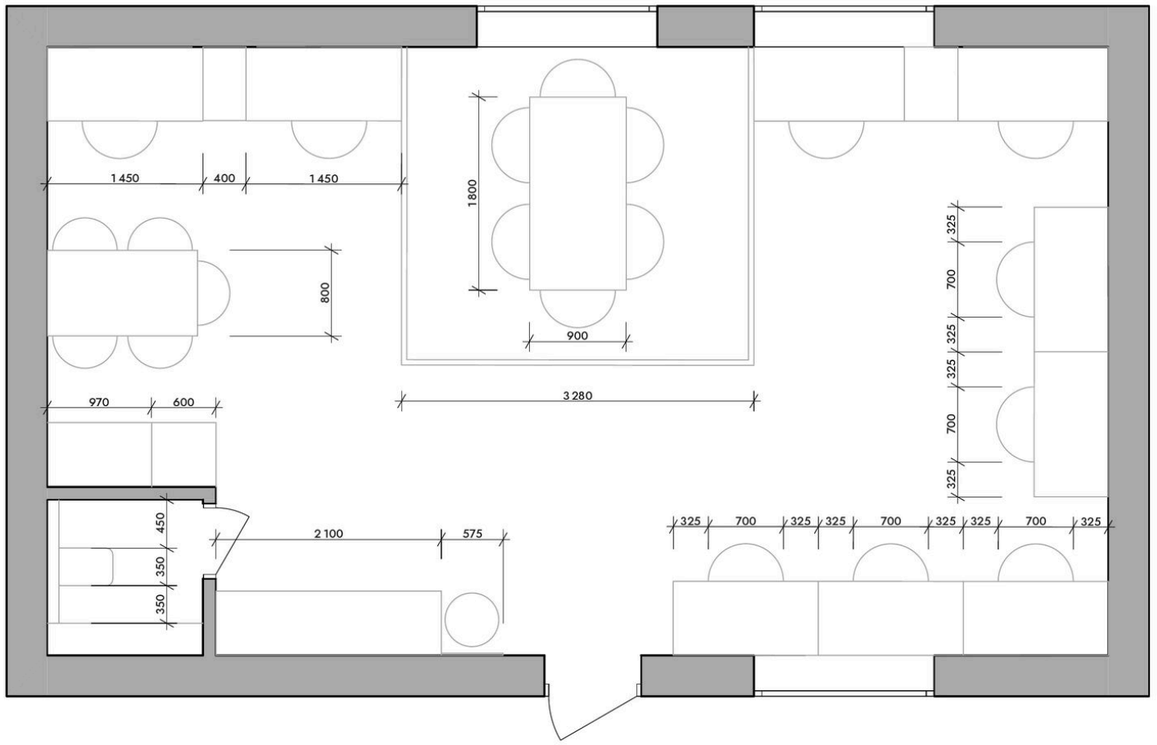

ПЛАН СВІТИЛЬНИКІВ
М 1:50

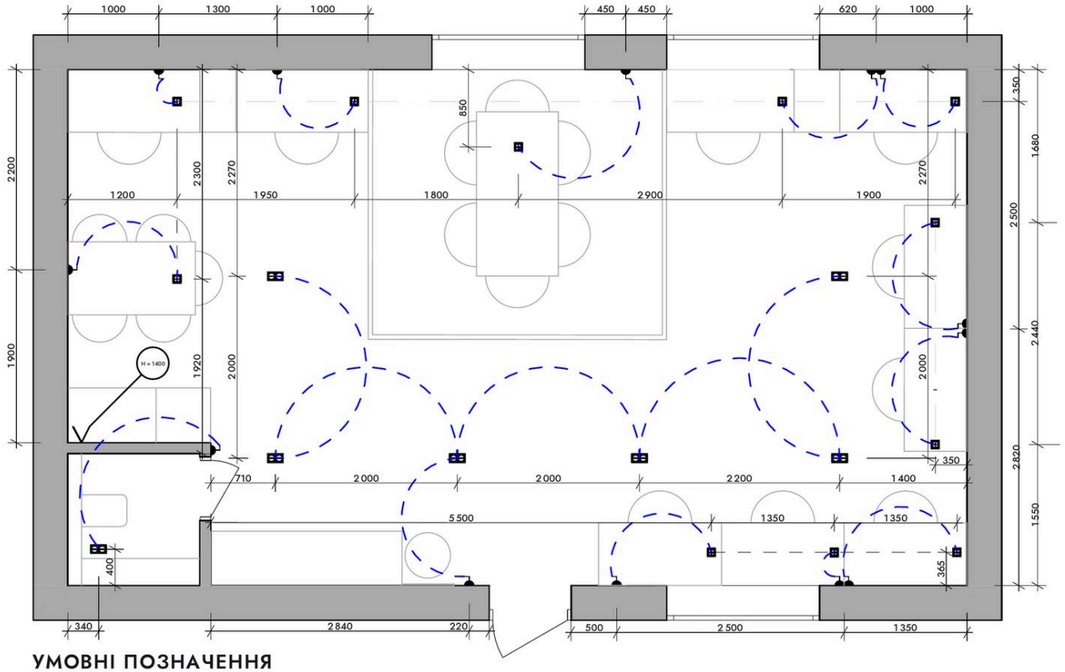


УМОВНІ ПОЗНАЧЕННЯ

вимикач
світильник точковий подвійний
світильник підвісний

ПРИМІТКИ

висота від чистої підлоги до центру вимикача 900 мм, крім висот вказаних на плані.


ПЛАН МОНТАЖНИХ І ДЕМОНТАЖНИХ РОБІТ
М 1:50

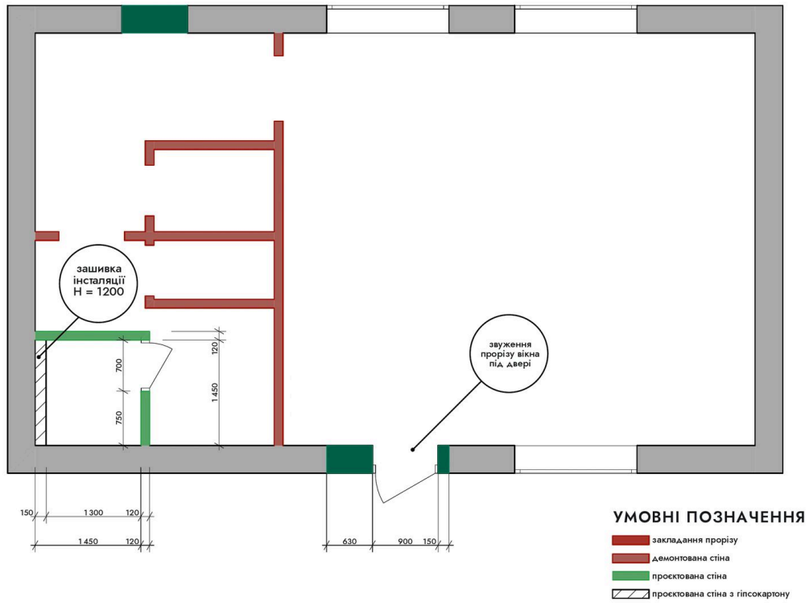

УМОВНІ ПОЗНАЧЕННЯ

- закладання прорізу
- демонтована стіна
- проєктована стіна
- проєктована стіна з гіпсокартону

ПЛАН РОЗЕТОК
М 1:50

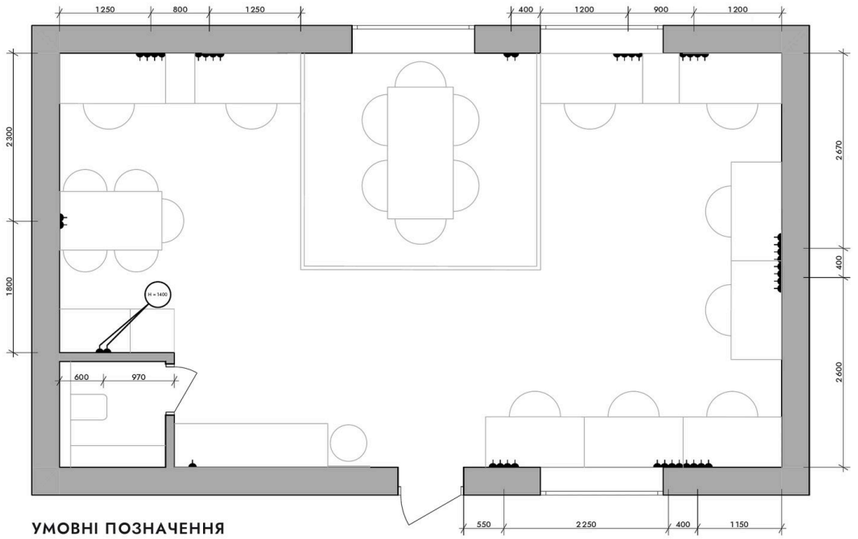


УМОВНІ ПОЗНАЧЕННЯ

- розетка

ПРИМІТКИ

висота від чистої підлоги до центру розетки 300 мм, крім висот вказаних на плані.

МЕБЛІ ІНДИВІДУАЛЬНОГО ВИГОТОВЛЕННЯ
М 1:25

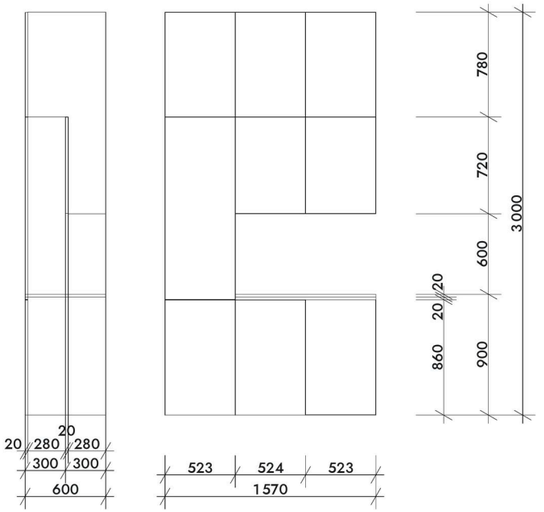



ДЯКУЮ ЗА УВАГУ

Більше проєктів, анімації та CV:

oleksandr-riznyk.vercel.app/ua/interior-designer

alexriznyk2004@gmail.com

+48 788 818 316 (WhatsApp)

LinkedIn · Telegram