PORTFOLIO · 2026



OLEKSANDR RIZNYK

Interior Designer

Interior concepts, space planning, materials and finishes, presented with photoreal visualization.

alexriznyk2004@gmail.com

+48 788 818 316 (WhatsApp)

LinkedIn · Telegram

oleksandr-riznyk.vercel.app/interior-designer



Interior Designer with a Bachelor's degree in Architecture and 2+ years of full-time experience. Developed interior concepts for residential and commercial spaces and designed furniture showrooms from concept to technical drawings. Prepares furniture layouts and lighting plans, selects materials and finishes, and presents ideas with photorealistic 3D visualization.

EXPERIENCE

CG Artist / 3D Designer

FRANKOF, furniture factory · May 2025 — July 2026

— Designed furniture showroom interiors with functional zones for different collections, from concept and visualization to technical drawings.
— Prepared design documentation: furniture layouts and planograms, lighting plans, built-in furniture, cabinetry and wall finishing plans.
— Provided design revisions and remote consultations during renovation and furniture installation.

Interior Designer / 3D Visualizer

MBA Development Group, remote · October 2024 — May 2025

— Developed interior design concepts for residential and commercial spaces, from first idea to visual presentation.
— Analyzed existing spaces and their potential to find functional design solutions.
— Selected color palettes, finishing materials, textures, furniture and decorative elements for cohesive interiors.

SKILLS

Interior concepts · Space planning · Showroom design · Materials and finishes · Color palettes · Furniture layouts · Lighting plans · 3D modeling · Reading architectural drawings · Archicad · 3ds Max · Corona Renderer · Adobe Photoshop

EDUCATION

Bachelor of Architecture

Ivano-Frankivsk National Technical University of Oil and Gas
2022 — 2026

LANGUAGES

Ukrainian (native), English (B1), Polish (B1)



01 / 06

LIVING ROOM WITH A GARDEN VIEW

A living room built around the view: floor-to-ceiling glazing onto a pine garden, oak-veneer wall panels with dark marble inserts, a lit stair and paper lanterns over the seating.

MY PART

Interior concept and scene: layout, materials, lighting, rendering. The furniture models were supplied.

MATERIALS

Oak-veneer wall panels, dark marble inserts, concrete ceiling, large stone-look floor tiles, jute rug, stone coffee table, suede-like upholstery.

LIGHTING

Daylight from the glazing, paper lantern pendants, recessed downlights, hidden LED strips under the wall panels and stair treads, a slim floor lamp.

SOFTWARE

3ds Max: scene and layout. Corona Renderer: materials, light, render. Photoshop: post-production.

Camera animations are on the site · Full project on the site ↗


LIVING ROOM WITH A GARDEN VIEW










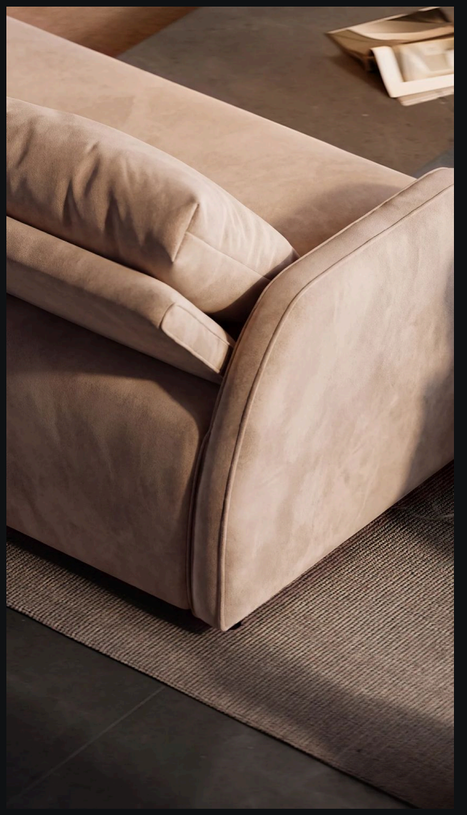

LIVING ROOM WITH A GARDEN VIEW

Clay and final

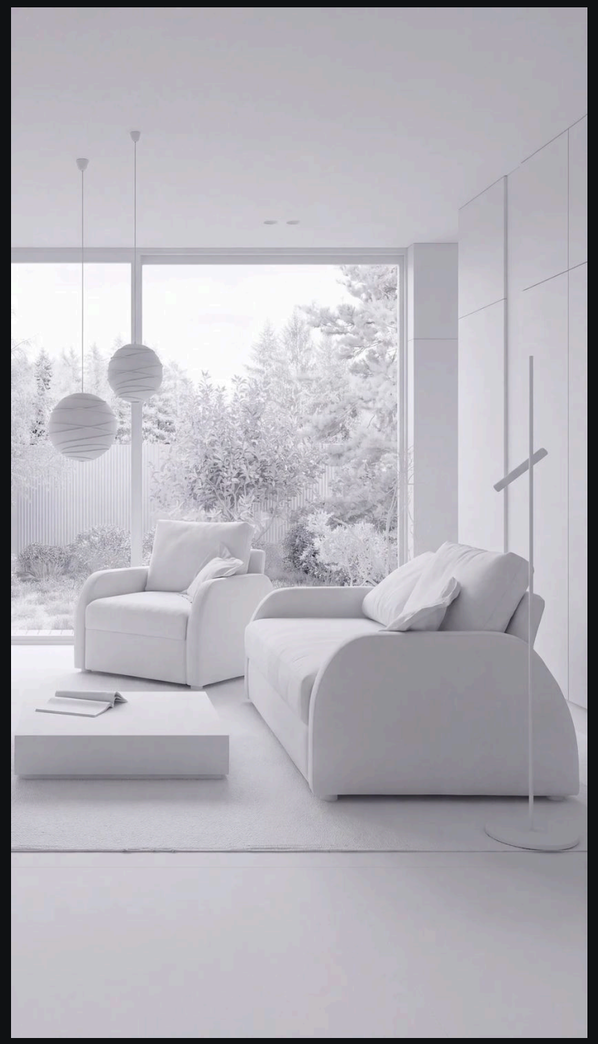






02 / 06

FRANKOF SHOWROOM

A furniture showroom for the FRANKOF factory, from the plan in 3ds Max to the built space. The hall is split into zones for bedroom, sofa, dining and lounge collections, with bookcase partitions carrying the brand.

MY PART

Showroom planning: zoning for collections, furniture layout and planograms, partitions and display elements, documentation for installation. Photos of the built showroom: FRANKOF.

MATERIALS

Black-stained ash bookcases with a backlit logo, timber-clad columns, dark curtains, graphite carpet, green accent wall.

LIGHTING

Black track spotlights on an open ceiling, floor lamps and table lamps inside the zones.

SOFTWARE

3ds Max: layout, planograms, presentation views. Archicad: drawings for wall colours, lighting and feature walls.

Full project on the site ↗









FRANKOF


FRANKOF
FRANKOF

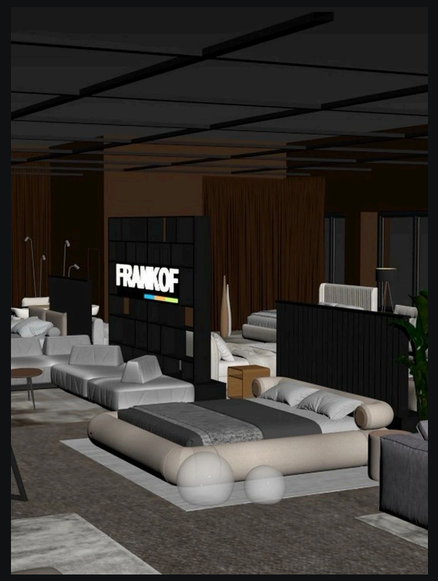
FRANKOF


FRANKOF
FRANKOF


FRANKOF



FRANKOF


FRANKOF
Історія FRANKOF розпочалась 8 жовтня 2009 року. За весь час
діяльності компанії ми непохитно переконались: ЛЮДИ - НАША
НАЙБІЛЬША ЦІННІСТЬ.
Ми вірємо, що справжня майстерність знаходиться в руках наших
працівників, адже на виробництві використовуємо не просто
фабричні станки, а й залучаємо українських майстрів, які слідкують
за кожним етапом створення виробів.
Ручна робота робить кожен виріб FRANKOF майстерним та
унікальним.
Завдяки турботі та досвіду нашої команди Ви інвестуєте у виріб, що
слугуватиме Вам роками.


FRANKOF


FRANKOF


WALL COLOURS

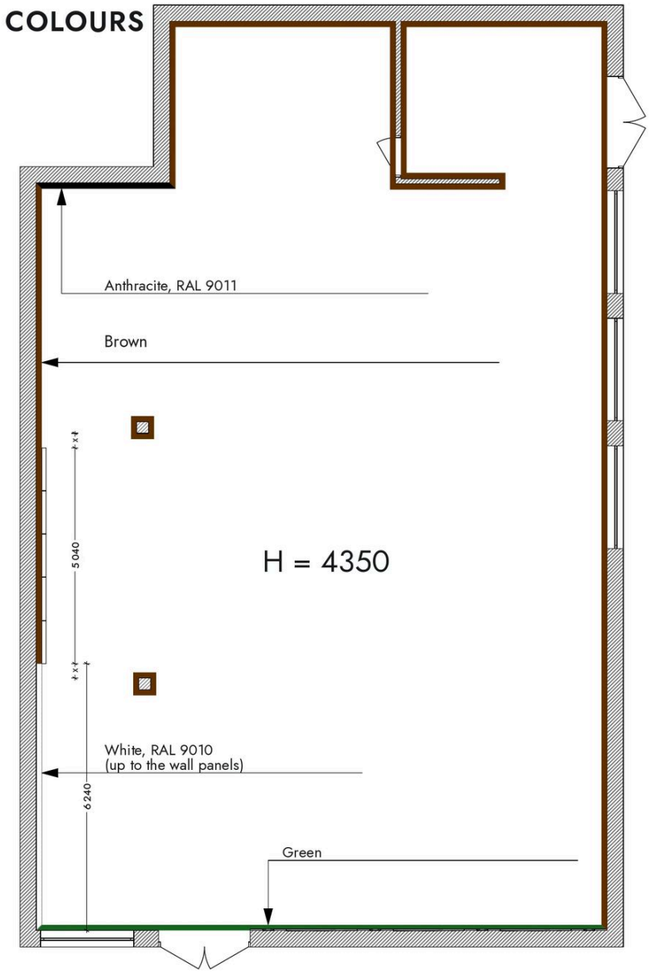

Green

Anthracite, RAL 9011

Brown

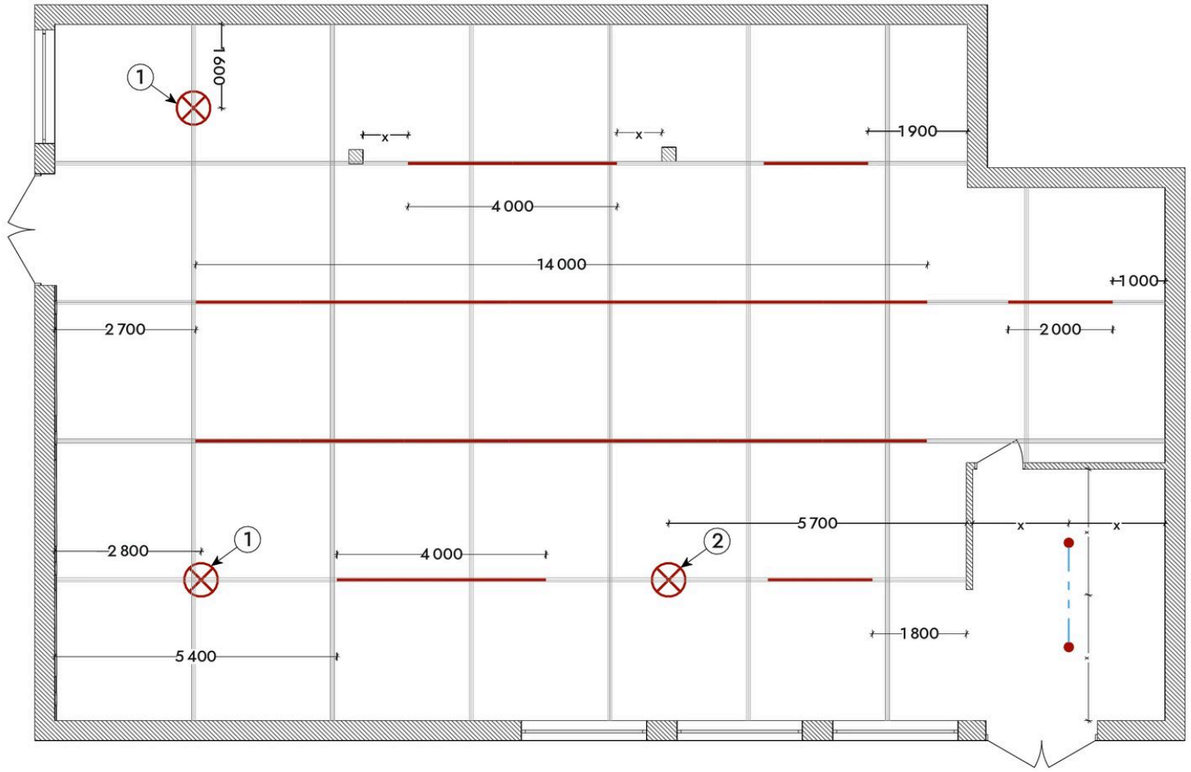

1



2



LIGHTING PLAN


Legend


pendant light

spotlight


track light

BRAND WALL ELEVATION

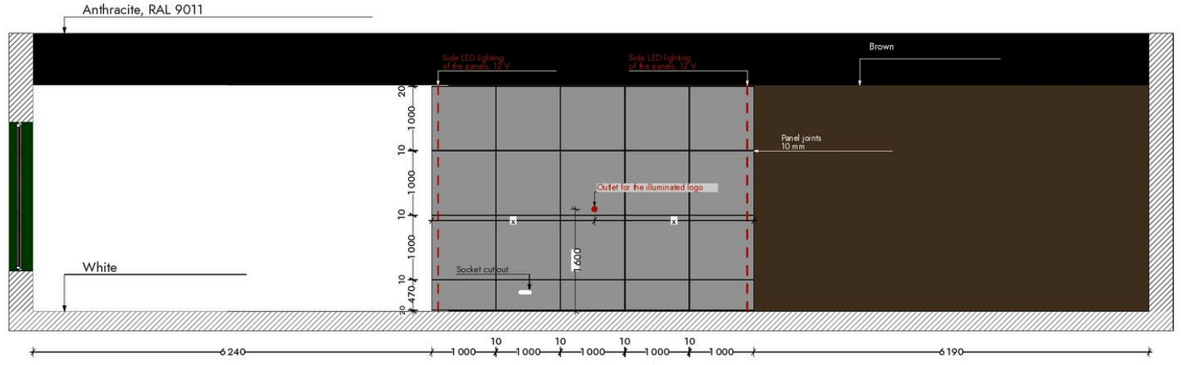

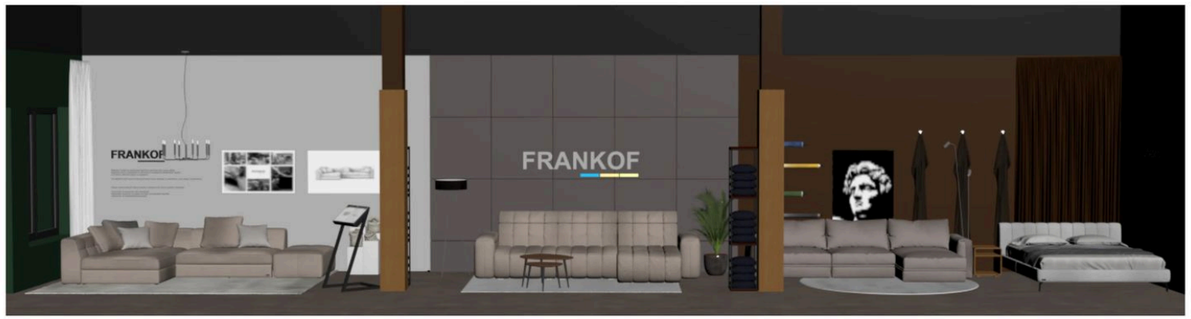

WALL WITH MOULDINGS

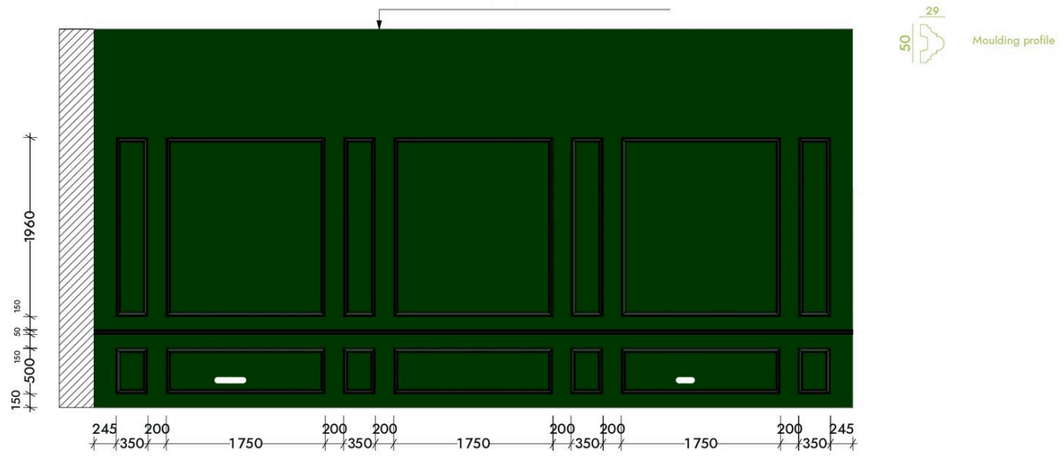





03 / 06

ATTIC APARTMENT

A whole apartment under a pitched roof, designed at MBA Development Group: kitchen and dining, living room with a fireplace, bedroom, study and bathroom in one calm, warm palette.

MY PART

Interior concept and visualization: zoning, materials and finishes, furniture and lighting selection, rendering. Working drawings were outside my part.

MATERIALS

Herringbone oak floor, light stone island, black-framed glass partitions, backlit dark wood panels, stone around the fireplace, green walls with wood in the study, beige plaster and walnut vanity in the bathroom.

LIGHTING


Daylight from roof windows, hidden LED lines in niches and panels, sculptural pendants over the dining table.

SOFTWARE

3ds Max: modeling and scene. Corona Renderer: materials, light, render. Photoshop: post-production.

Full project on the site ↗



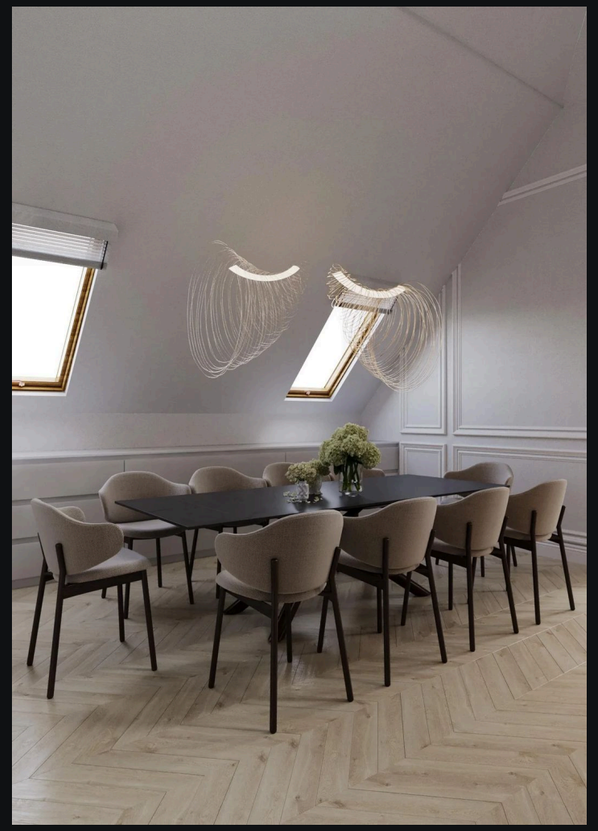


















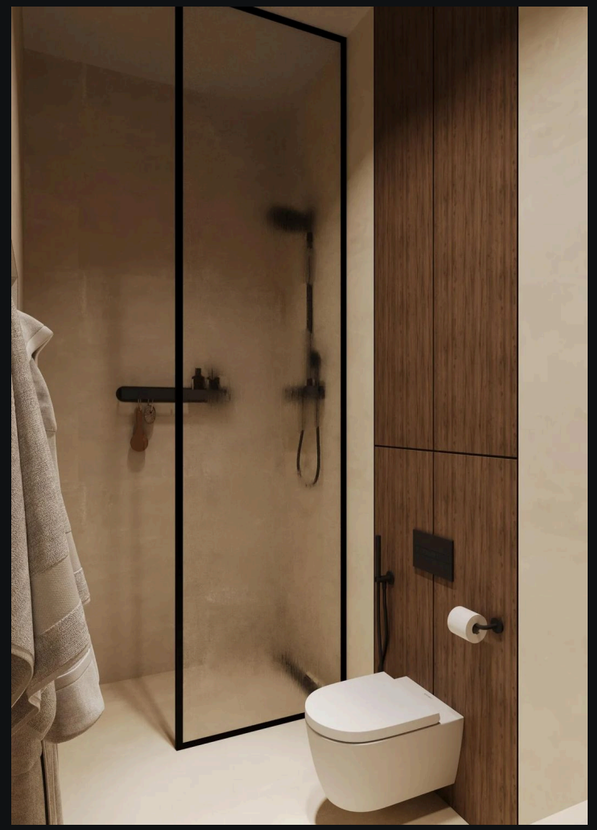





04 / 06

INTERIOR FOR A VELVET BED AND NIGHTSTAND

An upholstered bed and nightstand in a calm bedroom with timber panels and a marble band. One scene in two velvet colorways, plus the nightstand shot in five fabrics.

MY PART

Bed modeling, scene, materials, lighting, rendering, cinematic camera motion. The nightstand model was supplied.

MATERIALS

Upholstery: velvet (terracotta, gold, chocolate), ochre chenille, sand bouclé; dark oak wall panels with backlit stone inserts, marble band and marble floor tiles, linen bedding, wool rug.

LIGHTING

Soft daylight through sheer curtains, warm LED lines between the panels, two pendant lamps over the bed.

SOFTWARE

3ds Max: modeling and scene. Corona Renderer: materials, light, render. Photoshop: post-production. Cinematic camera motion from the stills.


Camera animations are on the site · Full project on the site ↗


INTERIOR FOR A VELVET BED AND NIGHTSTAND







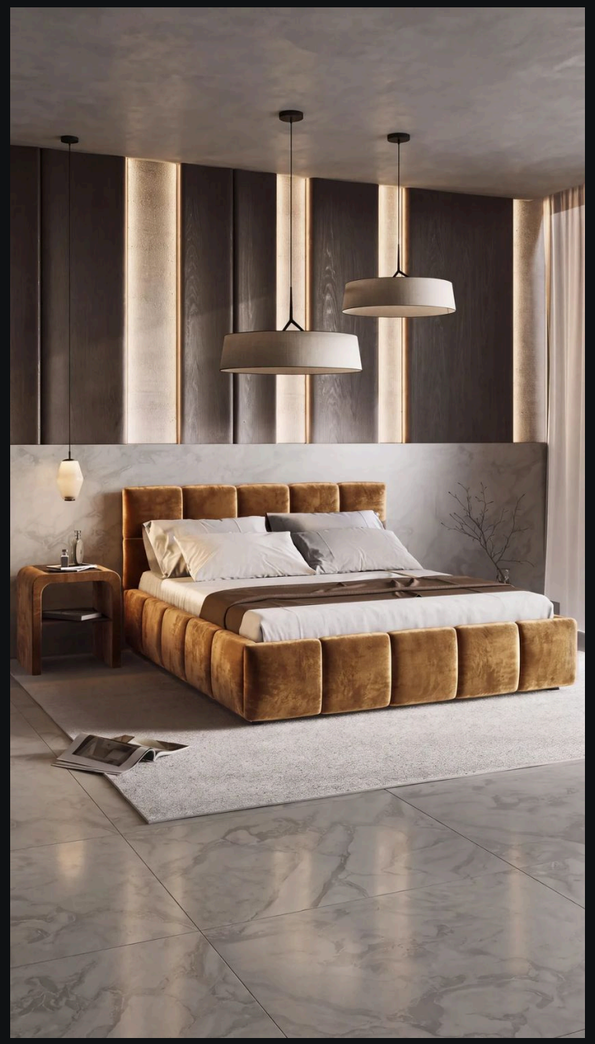

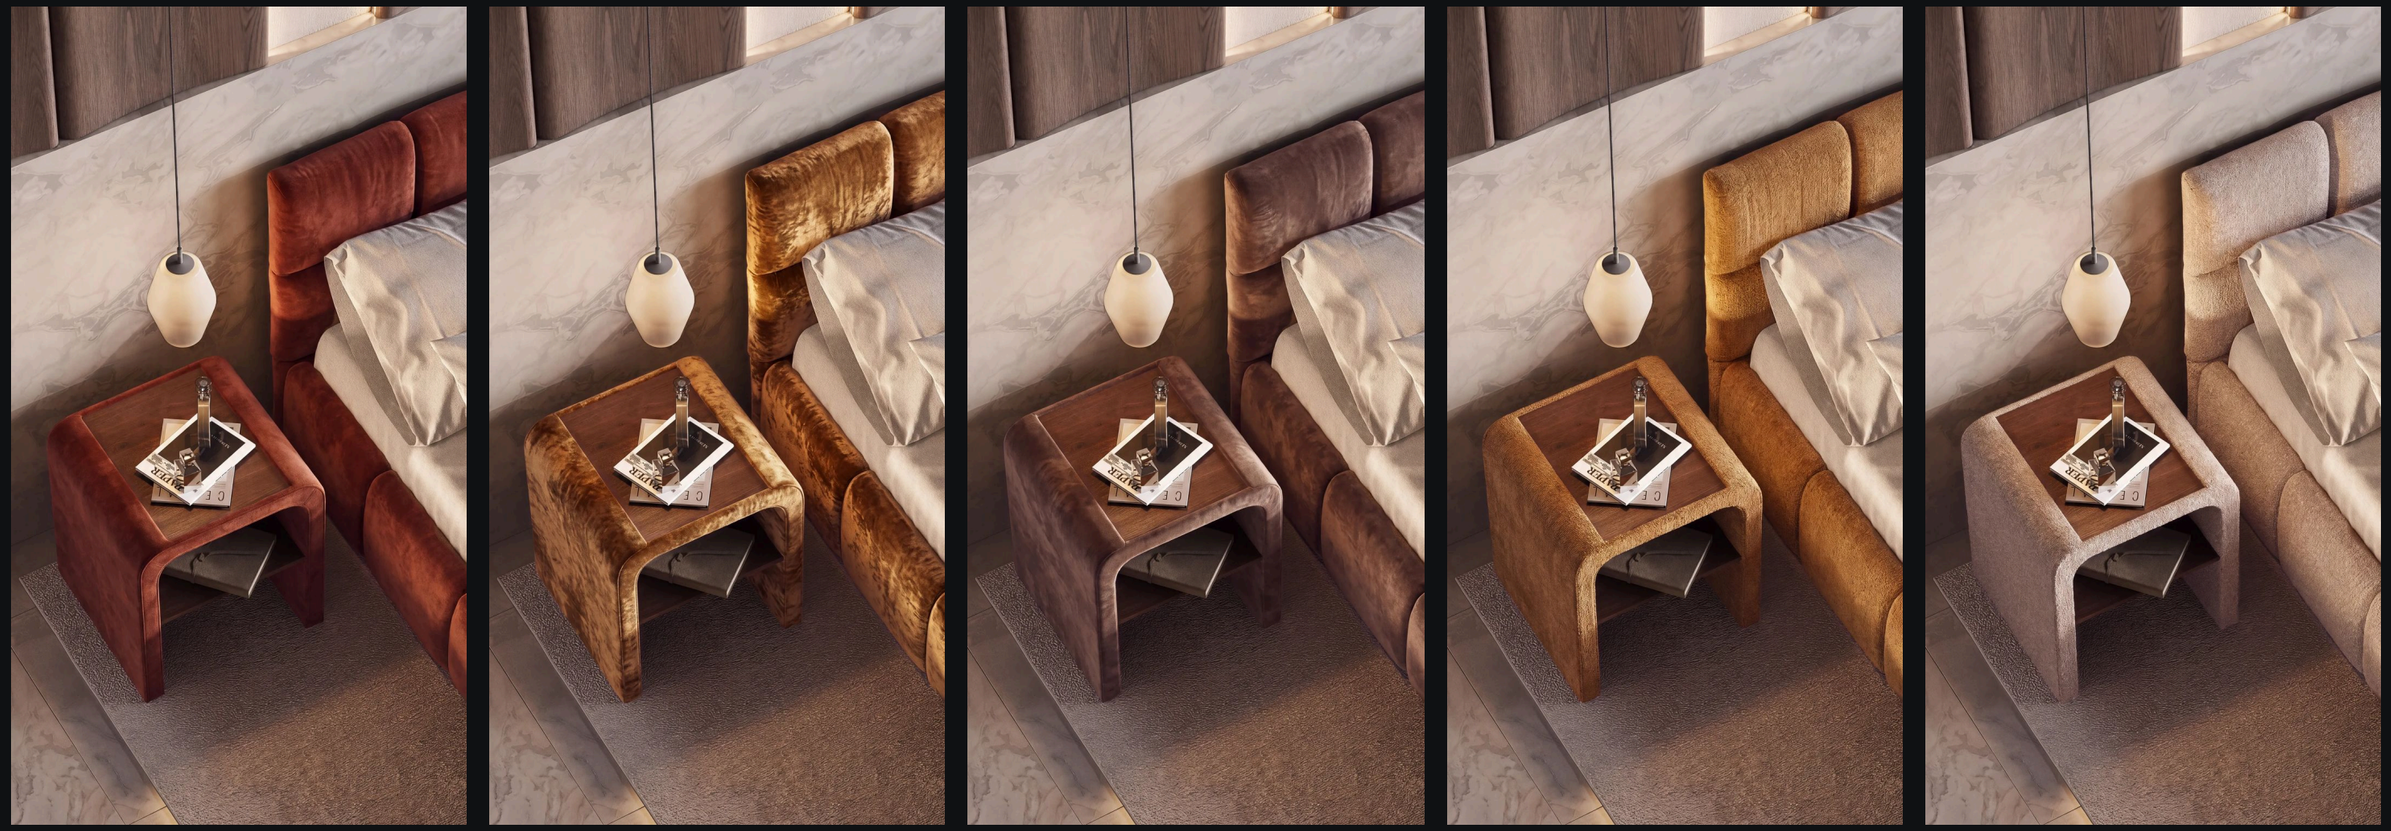



05 / 06

KITCHEN INTERIOR FOR BAR STOOLS

A bar stool presented in a kitchen I designed for it: travertine island, timber fronts and hidden linear light. The same shot carries five upholstery options.

MY PART

Kitchen interior concept and modeling, materials, lighting, rendering, cinematic camera motion. The stool model was supplied.

MATERIALS

Travertine island, wood-veneer fronts, concrete-look backsplash, oak floor, black metal legs. Upholstery: velvet, bouclé, faux fur, jacquard.

LIGHTING

Side daylight through blinds and a warm LED line under the wall cabinets.

SOFTWARE

3ds Max: kitchen modeling and scene. Corona Renderer: materials, light, render. Photoshop: post-production. Cinematic camera motion from the stills.

Camera animations are on the site · Full project on the site ↗











06 / 06

OFFICE

An office interior designed at MBA Development Group: a glass meeting room wrapped in a slatted timber partition, and an open workspace with a moss wall.

MY PART

Interior concept and visualization: zoning, materials, furniture, rendering. Working drawings were outside my part.


MATERIALS


Timber slats, frameless glass, light oak floor, moss wall, white desks.

SOFTWARE

3ds Max: modeling and scene. Corona Renderer: materials, light, render. Photoshop: post-production.


Full project on the site ↗

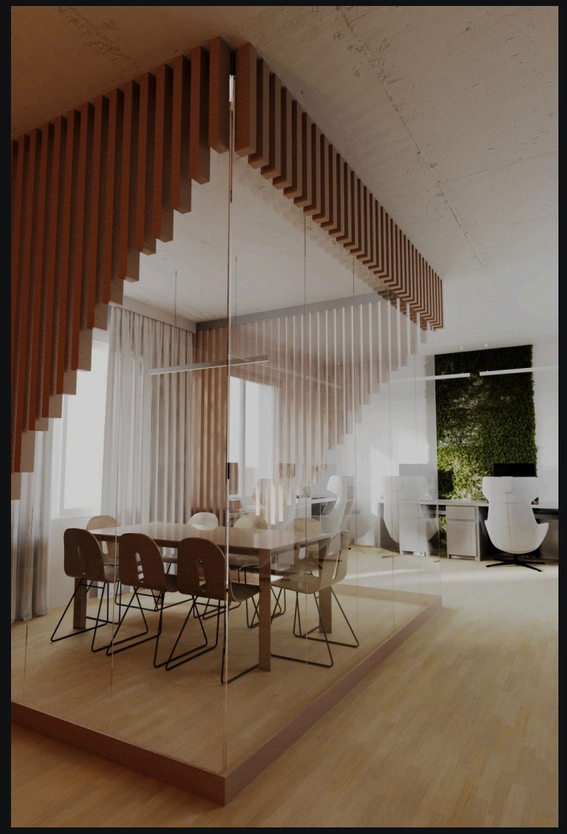

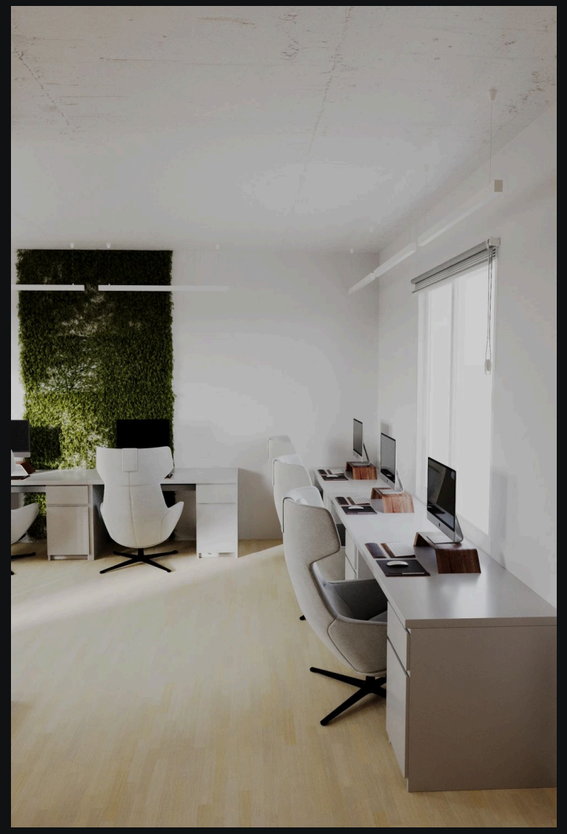




FURNITURE LAYOUT PLAN
SCALE 1:50

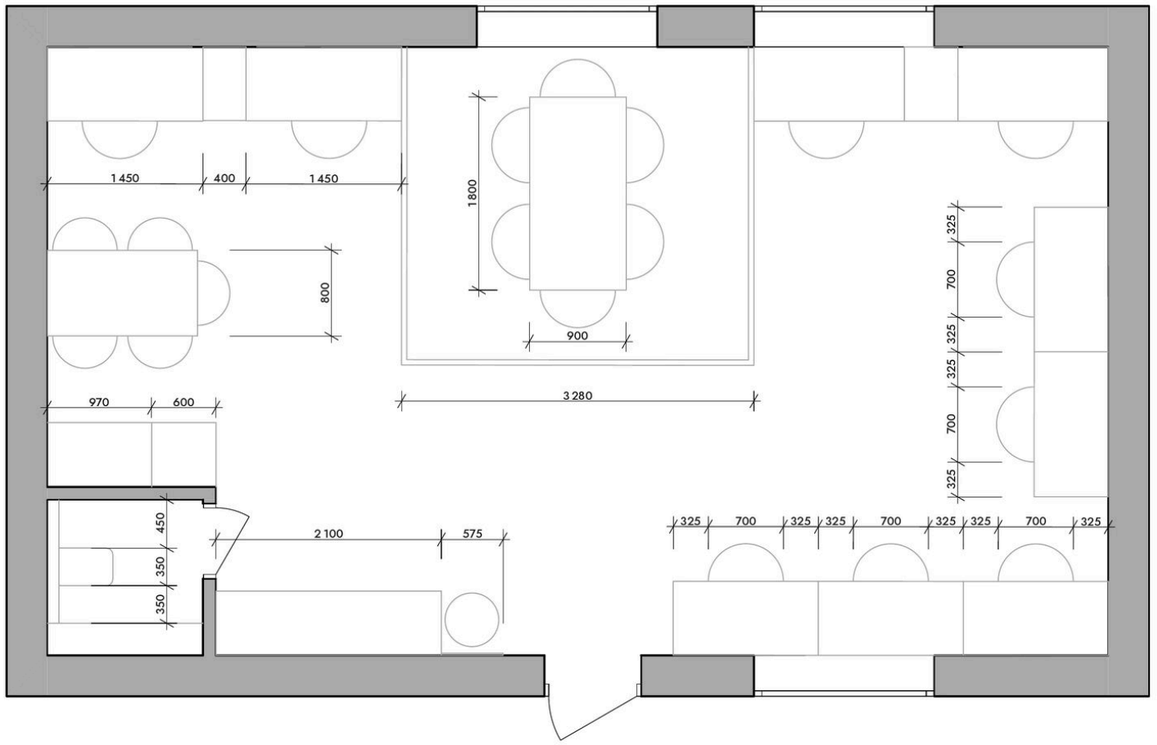

LIGHTING PLAN
SCALE 1:50

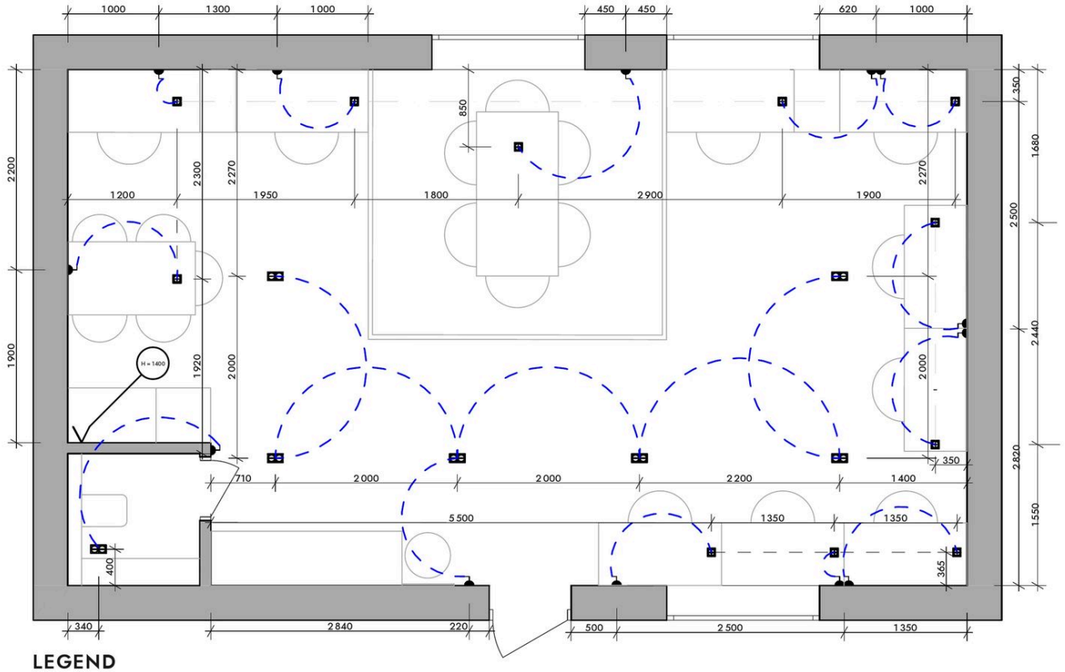


LEGEND

switch
double spotlight
pendant light


NOTES

switch centre height 900 mm above finished floor, unless a different height is shown on the plan.

CONSTRUCTION AND DEMOLITION PLAN
SCALE 1:50

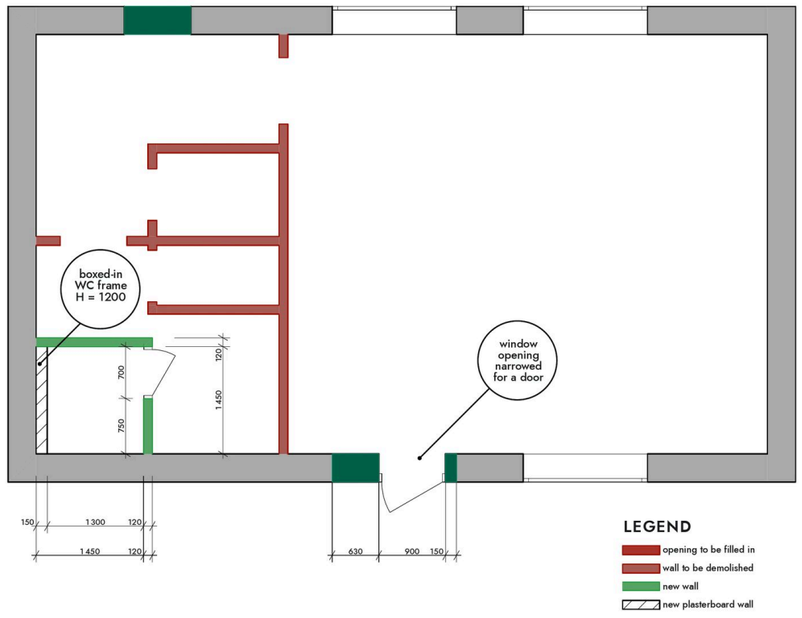

POWER SOCKET PLAN
SCALE 1:50

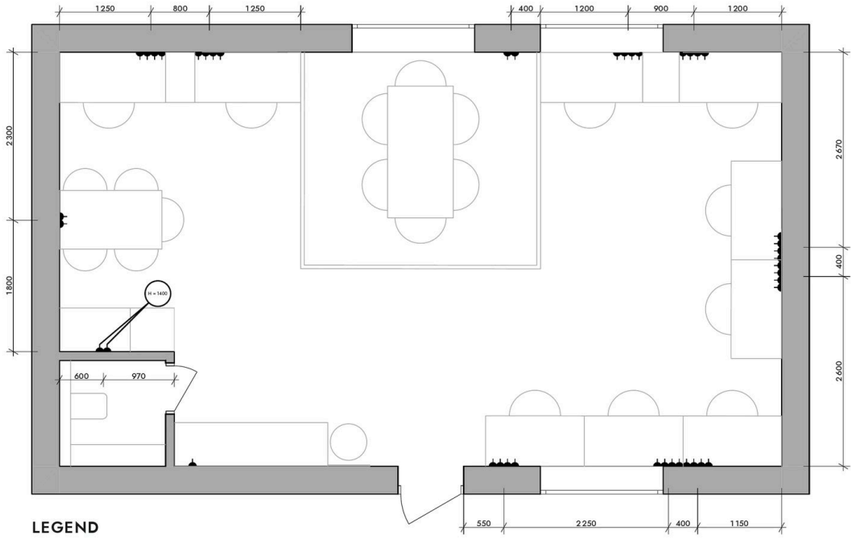


LEGEND

socket

NOTES

socket centre height 300 mm above finished floor, unless a different height is shown on the plan.

CUSTOM-MADE FURNITURE
SCALE 1:25

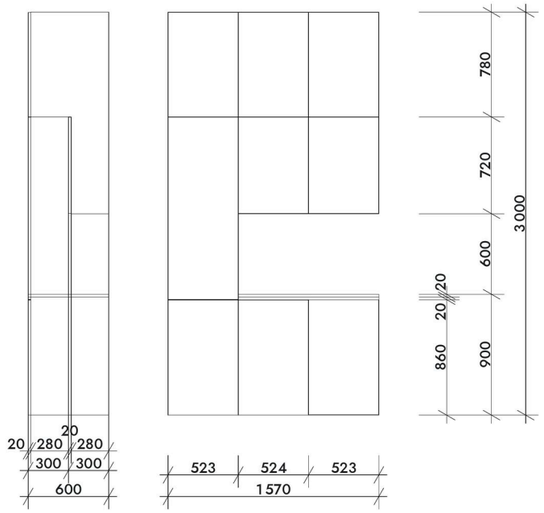



THANK YOU FOR YOUR TIME

More projects, animations and CVs:

oleksandr-riznyk.vercel.app/interior-designer

alexriznyk2004@gmail.com

+48 788 818 316 (WhatsApp)

LinkedIn · Telegram